



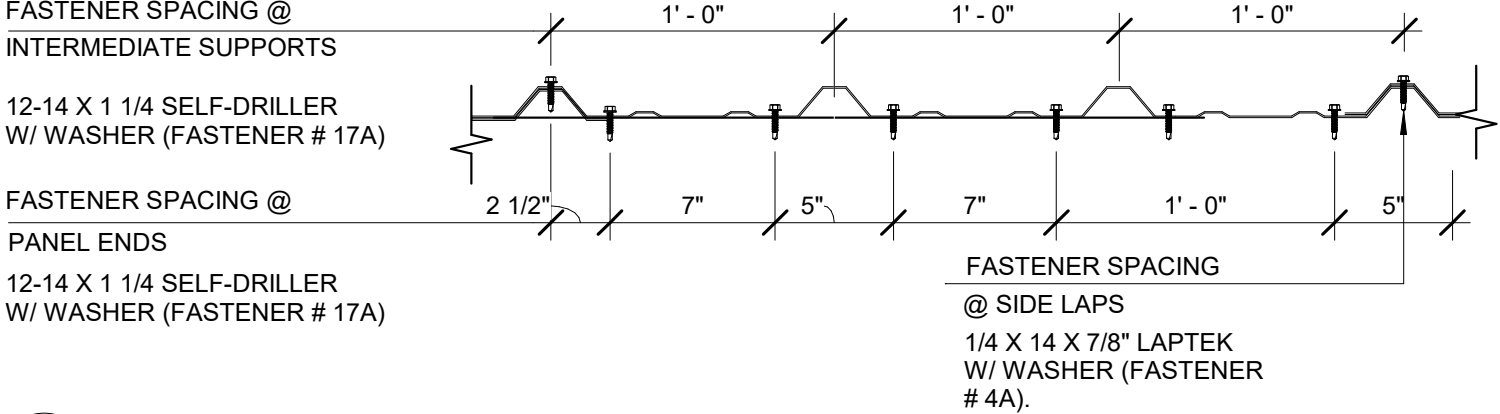

3 FASTENER SPACING DETAIL


GA-450 1 1/2" = 1'-0"

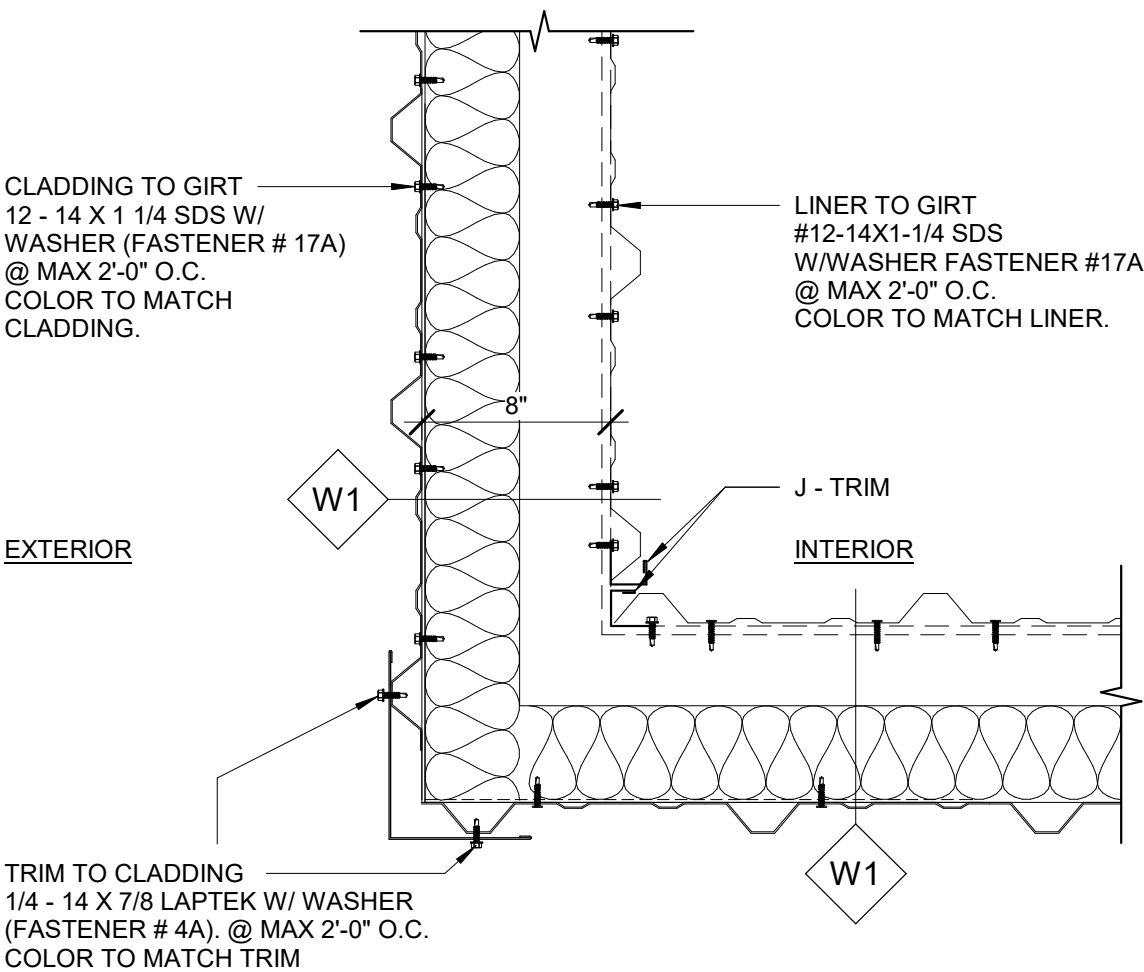

- NOTE:
- FOR CLADDING INSTALLATION REFER TO MANUFACTURER'S INSTALLATION MANUAL FOR TECHNICAL DATA AND INSTALLATION
 - TRIMS TO BE FASTENED AT A MAX. VERTICAL & HORIZONTAL SPACING OF 2'-0" O.C.
 - FOR TRIMS WHERE FASTENERS ARE HARDER TO INSTALL USE RIVETS AT A MAX VERTICAL OR HORIZONTAL SPACING OF 2'-0" O.C.

1 FASTENING DETAIL

GA-450 1 1/2" = 1'-0"

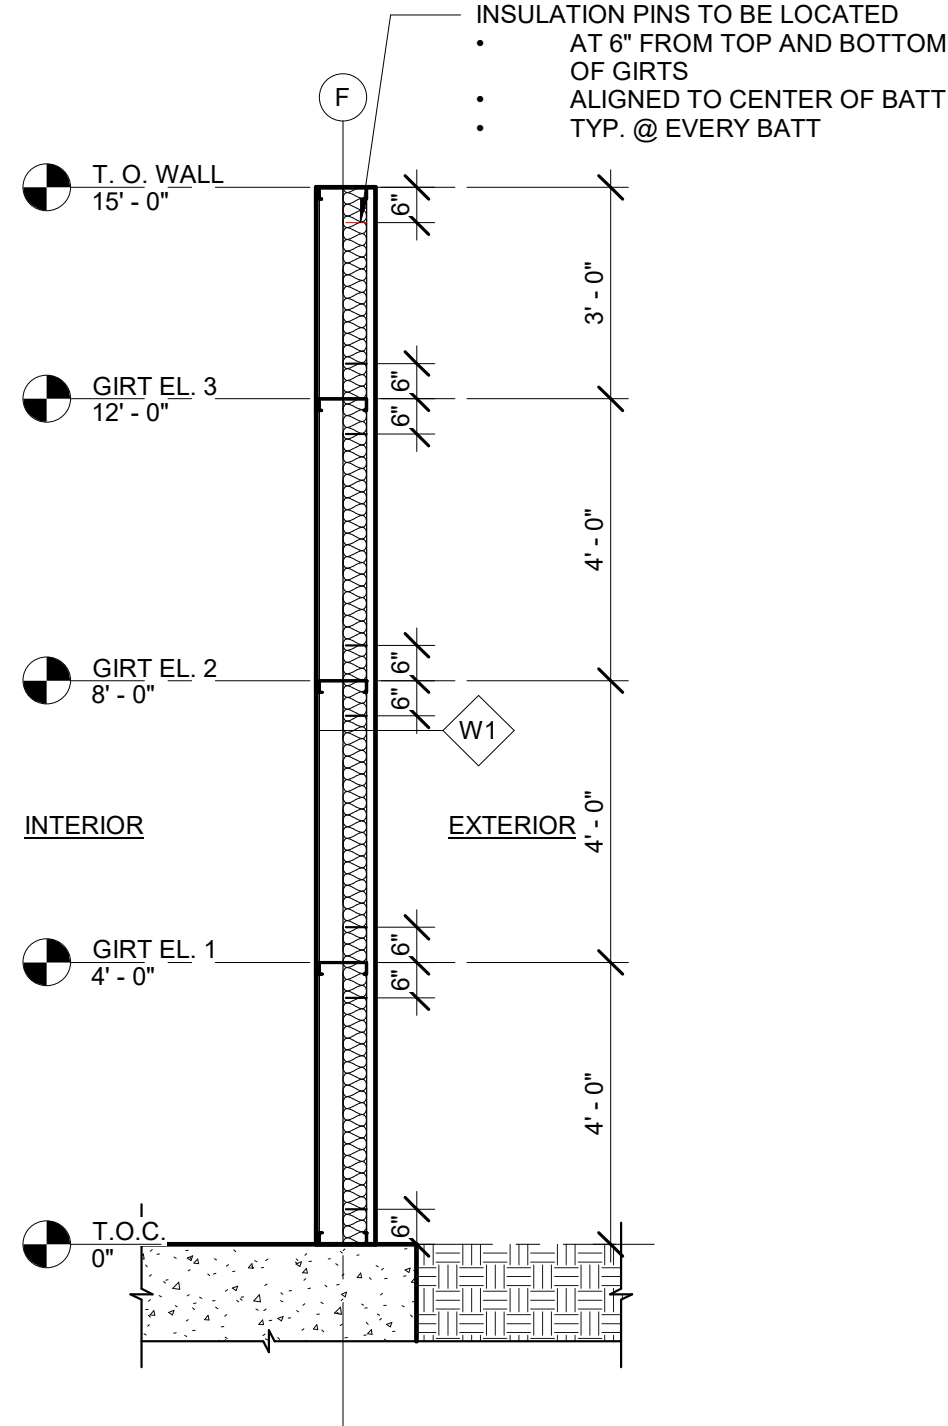

- NOTE:
- REFER TO MANUFACTURER'S MANUAL FOR TECHNICAL DATA AND INSTALLATION
 - INSULATION PINS TO BE LOCATED ON THE LOW RIBS OF THE CLADDING IN ORDER TO HAVE SUFFICIENT LENGTH TO SECURE PINS
 - MINIMUM 2 INSULATION PINS PER BATT OF INSULATION TO BE INSTALLAED (AT 6" TO TOP AND BOTTOM OF EACH GIRT)

2 INSULATION PIN DETAIL

GA-450 3/8" = 1'-0"

A	ISSUED FOR APPROVAL	06/08/2024
REVISIONS	DATE	

TVA CUMBERLAND
ACOUSTIC BARRIER WALL
PROJECT
TITLE
FASTENER DETAILS

CHKD	N.C.
DRAWN	R.S.
SCALE	As indicated
DATE DWN	02/27/24

SHEET #
GA-450

THE CONTRACTOR SHALL VERIFY ALL DIMENSIONS IN THE COURSE OF THE WORK. ANY DISCREPANCIES SHALL BE REPORTED TO THE COMMENCEMENT OF THE WORK UNDER NO CIRCUMSTANCES SHALL THE CONTRACTOR PROCEED IN UNCERTAINTY.

ALL INFORMATION CONTAINED WITHIN THIS DRAWING IS THE PROPERTY OF THE DRAWING ENGINEER. NO PART OF THIS DRAWING IS TO BE REPRODUCED OR TRANSMITTED IN ANY FORM OR BY ANY MEANS, ELECTRONIC OR MECHANICAL, WITHOUT THE WRITTEN PERMISSION OF THE DRAWING ENGINEER. THE USER AGREES TO ABIDE BY THESE TERMS AND CONDITIONS.

